GEK-45129B

INSTRUCTIONS

REFERENCE CARD
193X546ADG01

ELEMENTARY DIAGRAM	36C764188AD SH 1
CARD DIAGRAM	36C764188AD SH 2

REFER TO THE DRIVE SYSTEM INSTRUCTIONS AND ELEMENTARY DIAGRAMS FOR DESCRIPTIONS AND ADJUSTMENTS.

These instructions do not purport to cover all details or variations in equipment nor to provide for every possible contingency to be met in connection with installation, operation or maintenance. Should further information be desired or should particular problems arise which are not covered sufficiently for the purchaser's purposes, the matter should be referred to General Electric Company.

GENERAL ELECTRIC

GEK-45129A (2/84) 1M (P)

DRAWING NO.

CONT ON SHEET SH NO.

©

GENERAL ELECTRIC

36C764188AD
CONT ON SH 2 SH NO. 1

TITLE ELEMENTARY DIAGRAM
REFERENCE CARD
FIRST MADE FOR STD LINE
193X546ADG01

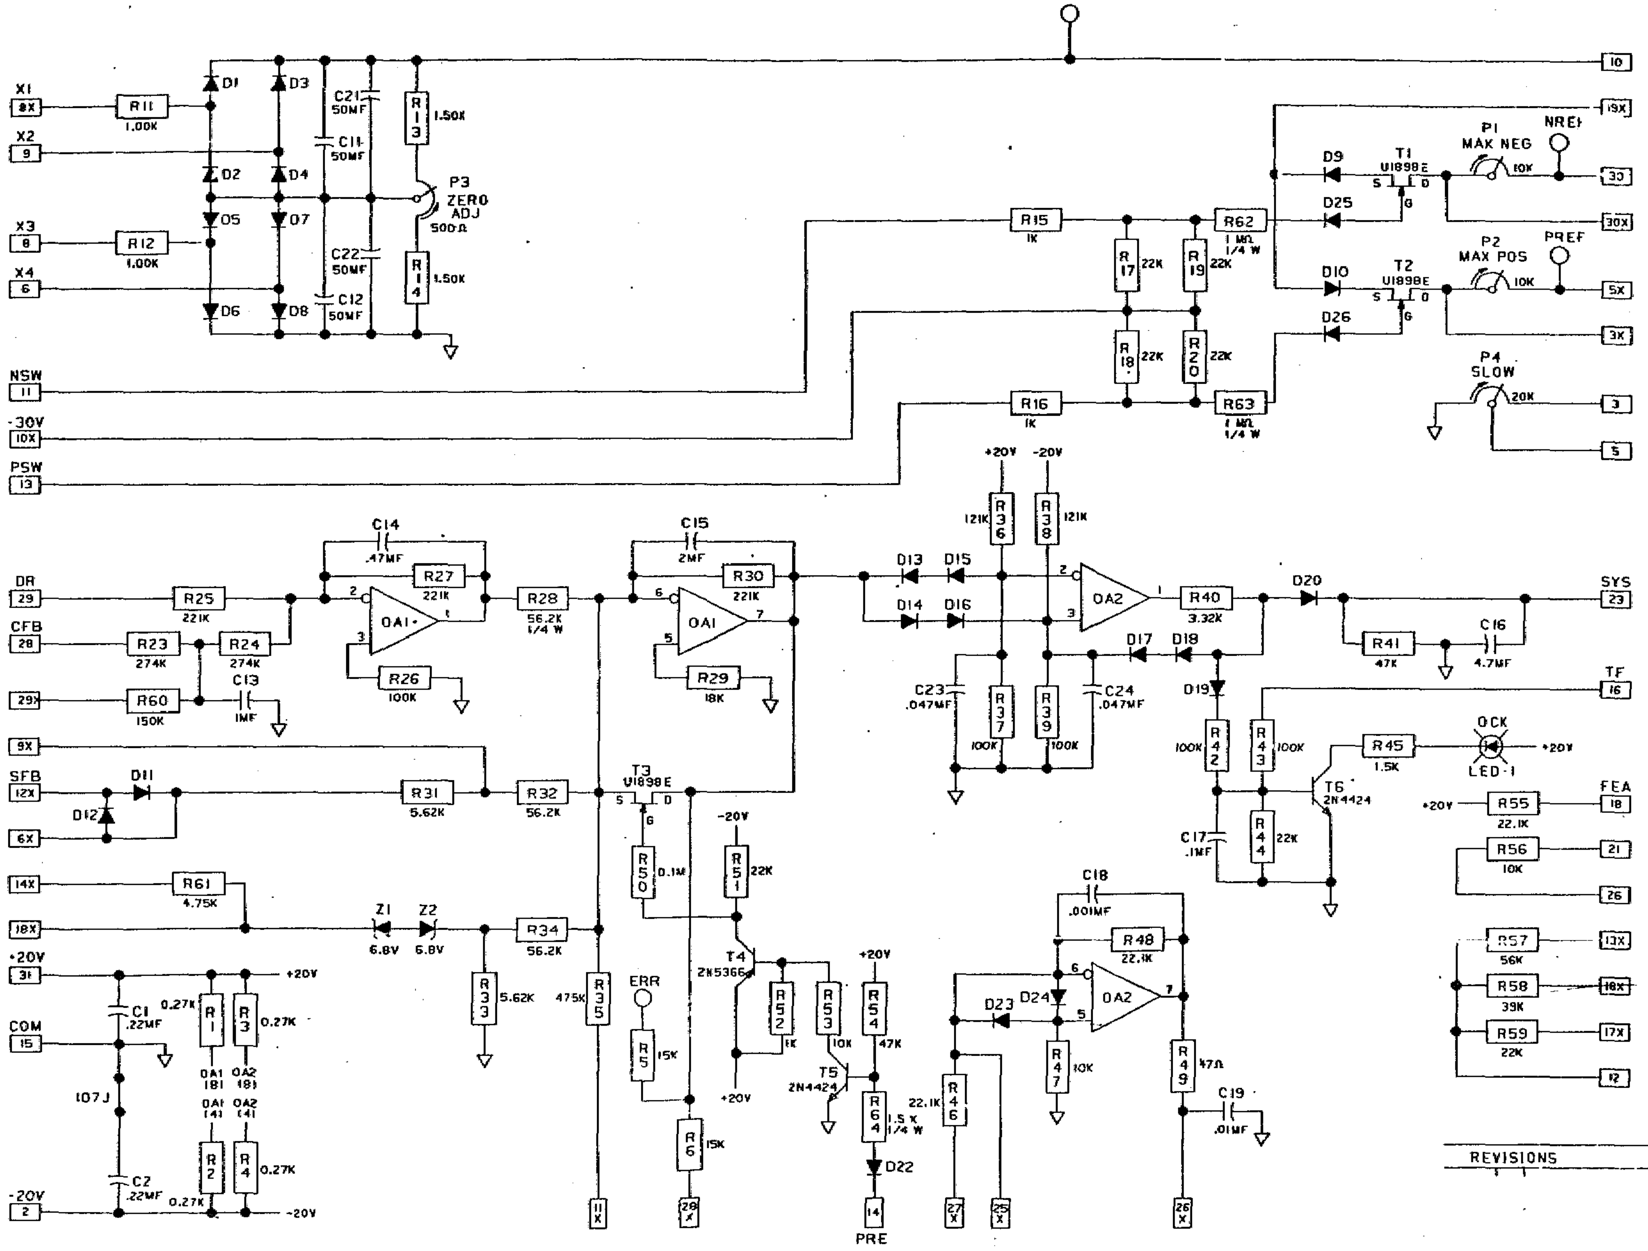

REVNO
0

REVISIONS

PRINTS TO	
5B(B1W)	JA(CD)
SR(2)BW	5J(BW)
SL(2)BW	STS(SO)
AW(BW)	SE(A&S)
5D(CD)	SP(1)BW
5D(BK)	CAD

NO REVISIONS ARE TO BE MADE TO THIS DRAWING WITHOUT THE SPECIFIC APPROVAL OF THE DEVELOPMENT ENGINEERING SUB-SECTION OF THE SPEED VARIATOR PRODUCTS OPERATION.

MADE BY D LANICH OCT.31,1983
ISSUED D Lanich Jan. 26, 1984
APPROVALS

SPEED VARIATOR PROD. DIV OR DEPT.
ERIE, PA. LOCATION

36C764188AD
CONT ON SH 2 SH NO. 1

GENERAL ELECTRIC

UNLESS OTHERWISE SPECIFIED USE THE FOLLOWING				
APPLIED PRACTICES	SURFACES	TOLERANCES ON MACHINED DIMENSIONS		
718A515	✓	±	±	±

TITLE PRINTED CIRCUIT DIAGRAM

, REFERENCE CARD

FIRST MADE FOR STANDARD LINE

193X546AD G01

36C764188AD
CONT ON SHEET FL SH NO 2

~~HOLE TABULATION~~		
~~ALL HOLES 040 DIA EXCEPT THE HOLES TABULATED BELOW~~		
~~LOC.~~	~~DIA~~	~~QUAN.~~
~~A~~	~~.157~~	~~2~~
~~B~~	~~.032~~	~~32~~
~~C~~	~~.081~~	[illegible]

DO NOT USE- SEE DRILL & TRIM DWG # 36A398485AA

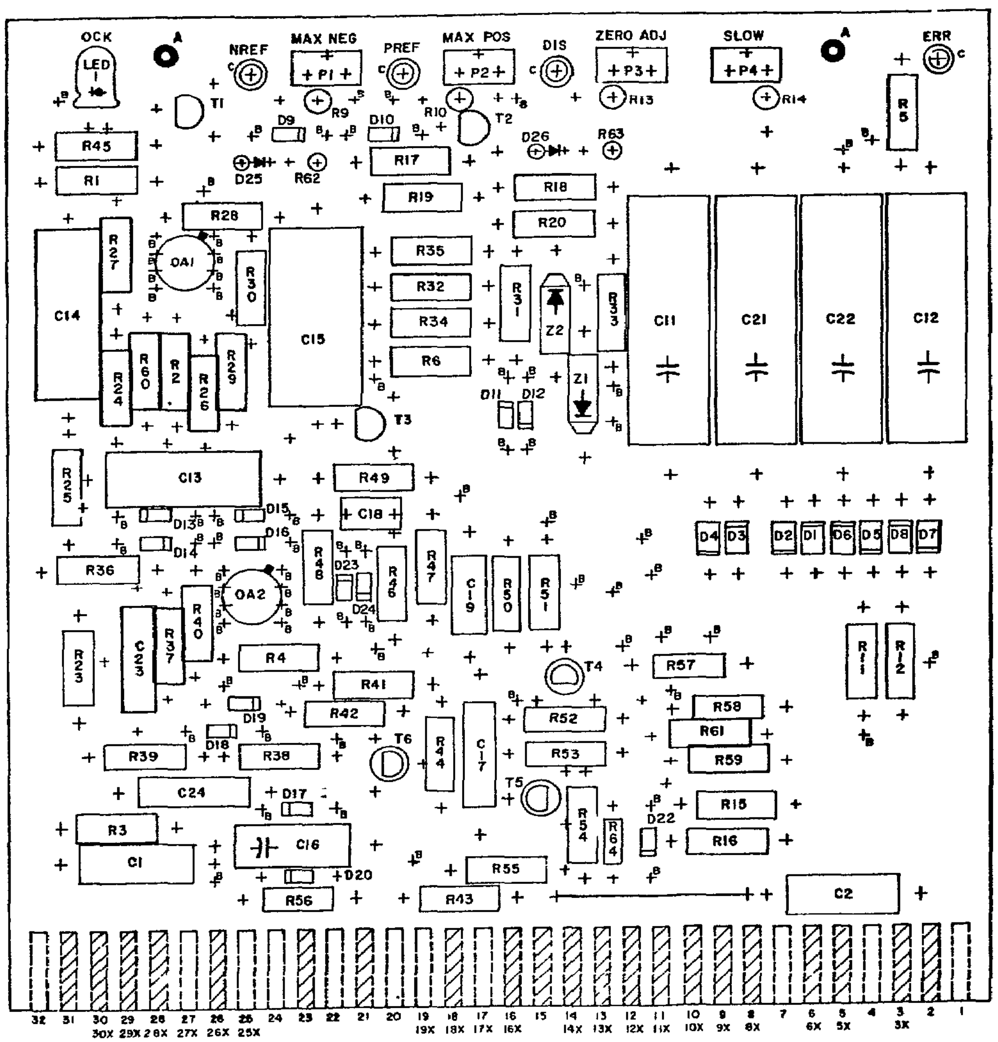

SEE NOTE 1,2,&4

GROUP	KEY LOCATIONS			
1	4—5	12—13	22—23	———

NOTES

1. INDICATED TAB NUMBERS CORRESPOND TO MATCHING RECEPTACLE NUMBERS
2. CROSS HATCHED TABS INDICATES TABS USED.
3. CARD SIZE, $5.500^{+.000}_{-.015}$ X $5.130^{+.002}_{-.008}$
4. THIS CARD HAS GOLD PLATED TABS ON BOTH SIDES. TABS 1 THRU 32 ARE LOCATED ON THE REVERSE SIDE. TABS 1X THRU 32X ARE LOCATED ON THE COMPONENT SIDE OF THE CARD TAB 1X IS OPPOSITE TAB 1 AND ETC. THE TAB NUMBERS SHOWN ARE THOSE USED ON THIS CARD

LEAD SKETCHES

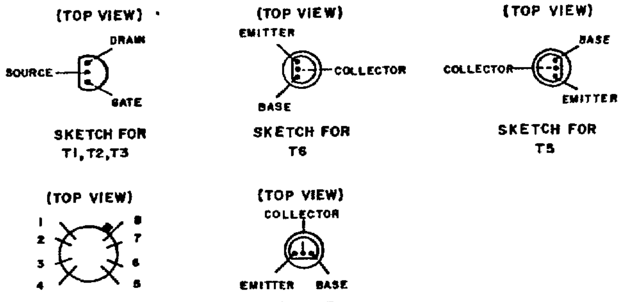

SKETCH FOR T1,T2,T3

SKETCH FOR T6

SKETCH FOR T5

SKETCH FOR OA1,OA2

SKETCH FOR T4

COMPONENT HEIGHT SKETCH
TRANSISTOR
(SIDE VIEW)

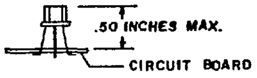

2X	36A358087AD005	36A358088AD005	1	———
SCALE	REAR ETCHED BOARD DWG.	FRONT ETCHED BOARD DWG.	FRONT	BACK
			SPACE UNIT REQUIREMENT	

REVISIONS

No revisions are to be made to this drawing without the specific approval of the Development Engineering Section of the Speed Variator Department

PRINTS TO	
5B(8)M	5J(9W)
5P(2)3W	5TS(50)
5L(2)BW	5E(ABS)
A W(3	5P(1)BW
5D(CD)	5D(BK)
[illegible]	

MADE BY P. Lamack OCT 28, 1983 ISSUED D. Lamack JAN. 26, 1984	APPROVAL	SPEED VARIATOR ERIE	36C764188AD CONT ON SHEET FL SH NO 2