INSTRUCTIONS

HOIST CARD

193X547ABG01

ELEMENTARY DIAGRAM	36C764190AB SH 1
CARD DIAGRAM	36C764190AB SH 2

REFER TO THE DRIVE SYSTEM INSTRUCTIONS AND ELEMENTARY DIAGRAMS FOR DESCRIPTIONS AND ADJUSTMENTS.

These instructions do not purport to cover all details or variations in equipment nor to provide for every possible contingency to be met in connection with installation, operation or maintenance. Should further information be desired or should particular problems arise which are not covered sufficiently for the purchaser's purposes, the matter should be referred to General Electric Company.

GENERAL ELECTRIC

36C764190AB
CONT ON SH 2 SH NO 1

TITLE ELEMENTARY DIAGRAM
HOIST CARD
FIRST MADE FOR STD LINE
193X547ABG01

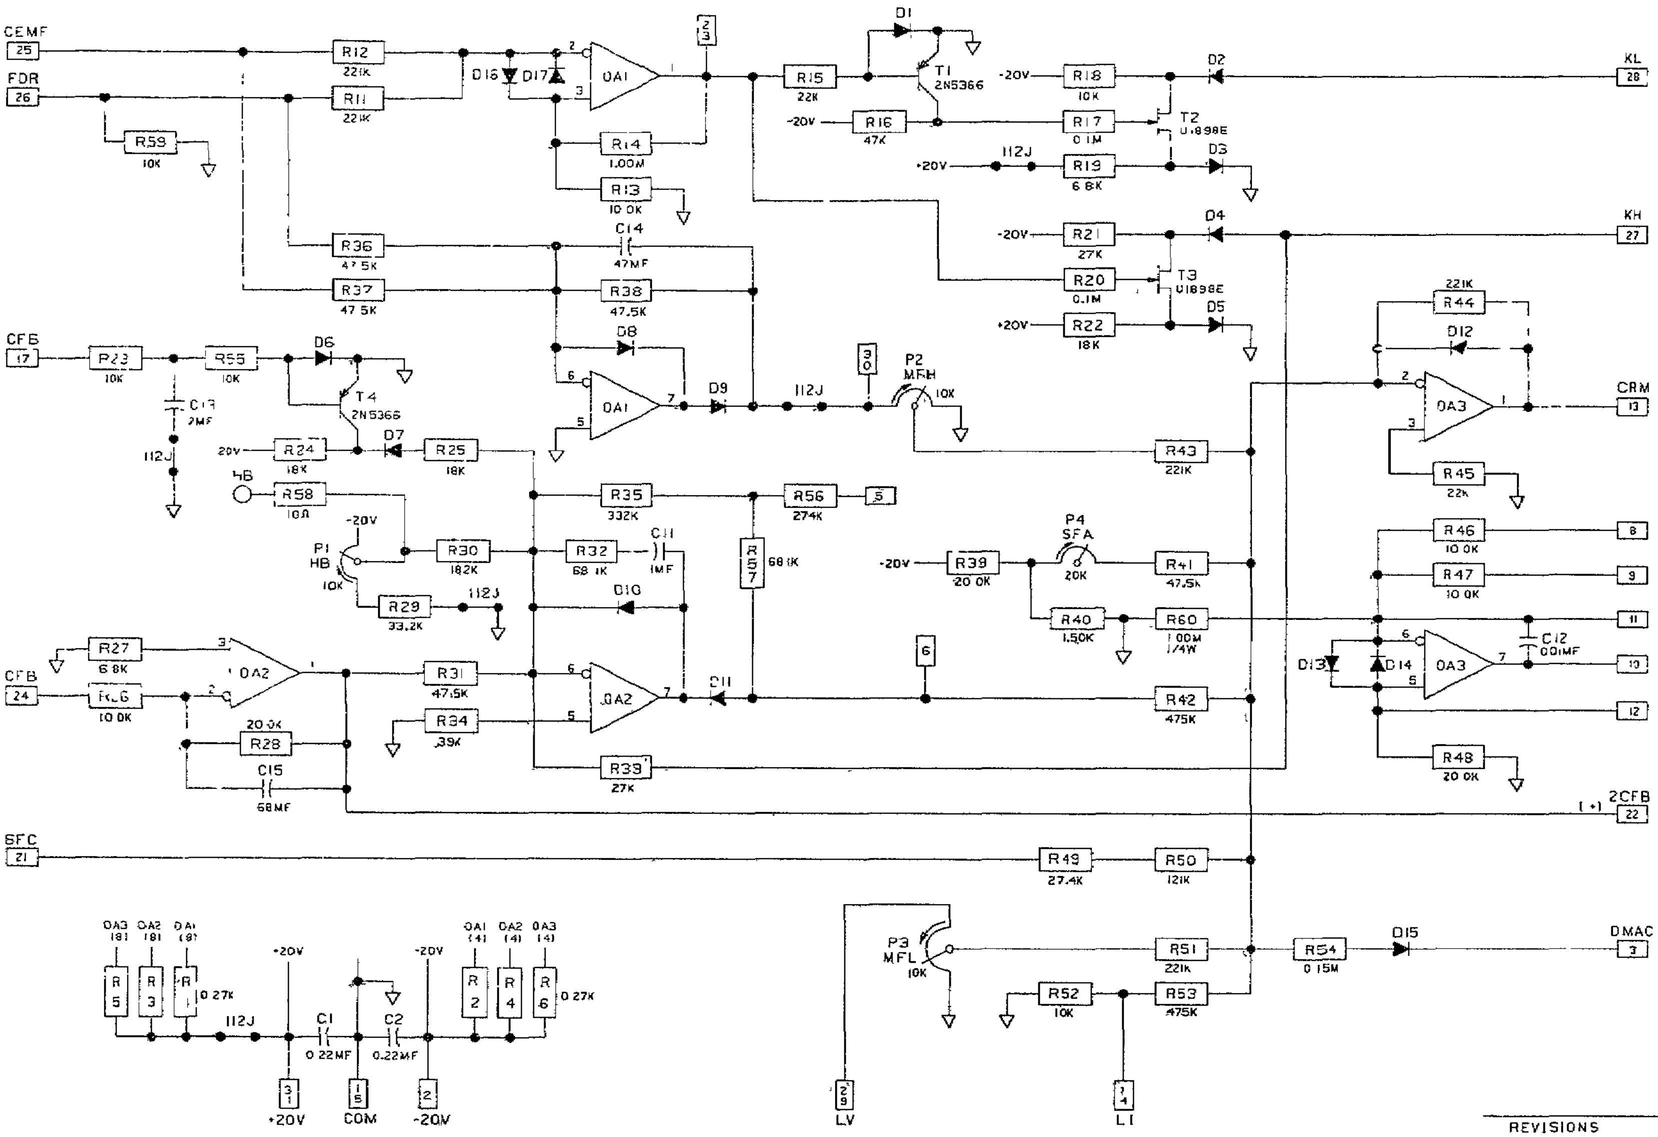

NOTES:
1 ALL DIODES ARE 1N4148
2 ALL OP AMPS ARE 1558

REV 0

REVISIONS

PR NTS TO	
55.8 M	JA.CC
SR 2.9W	SJ.BI
5L 2.6W	STS(5C
AW 3W	
SC(CO)	
SC 3K	CAD

NO REVISIONS ARE TO BE MADE TO THIS DRAWING WITHOUT THE SPECIFIC APPROVAL OF THE DEVELOPMENT ENGINEERING SUB-SECTION OF THE SPEED VARIATOR PRODUCTS OPERATION

MADE BY S J.HOLSOPPLE FEB 8,1984
ISSUED D Lancet MAY 9,1984
APPROVALS

SPEED VARIATOR PROD DIV OR DEPT
ERIE, PA LOCATION

36C764190AB
CONT ON SH 2 SH NO 1

DRAWING NO
CONT ON SHEET SH NO

FF 409 F I

GENERAL ELECTRIC

PRINTED CIRCUIT DIAGRAM
HOIST CARD
FIRST MADE OF STANDARD LINE
193X547ABG01

36 4190AB
SH NO 2

UNLESS OTHERWISE SPECIFIED USE THE FOLLOWING

APPLIED PRACTICES	SURFACES	TOLERANCES ON MACHINED DIMENSIONS		
		FRACTIONS	DECIMALS	ANGLES
718A515	✓	±	±	±

~~HOLE TABULATION~~

~~ALL HOLES .040 DIA EXCEPT THE HOLES TABULATED BELOW~~

~~LOC.~~	~~DIA.~~	~~QUAN~~
~~A~~	~~.157~~	~~2~~
~~B~~	~~.032~~	~~58~~
~~C~~	~~.081~~	~~1~~

FOR PROPER DRILLING INFORMATION SEE DRILL AND TRIM 36A398579AA

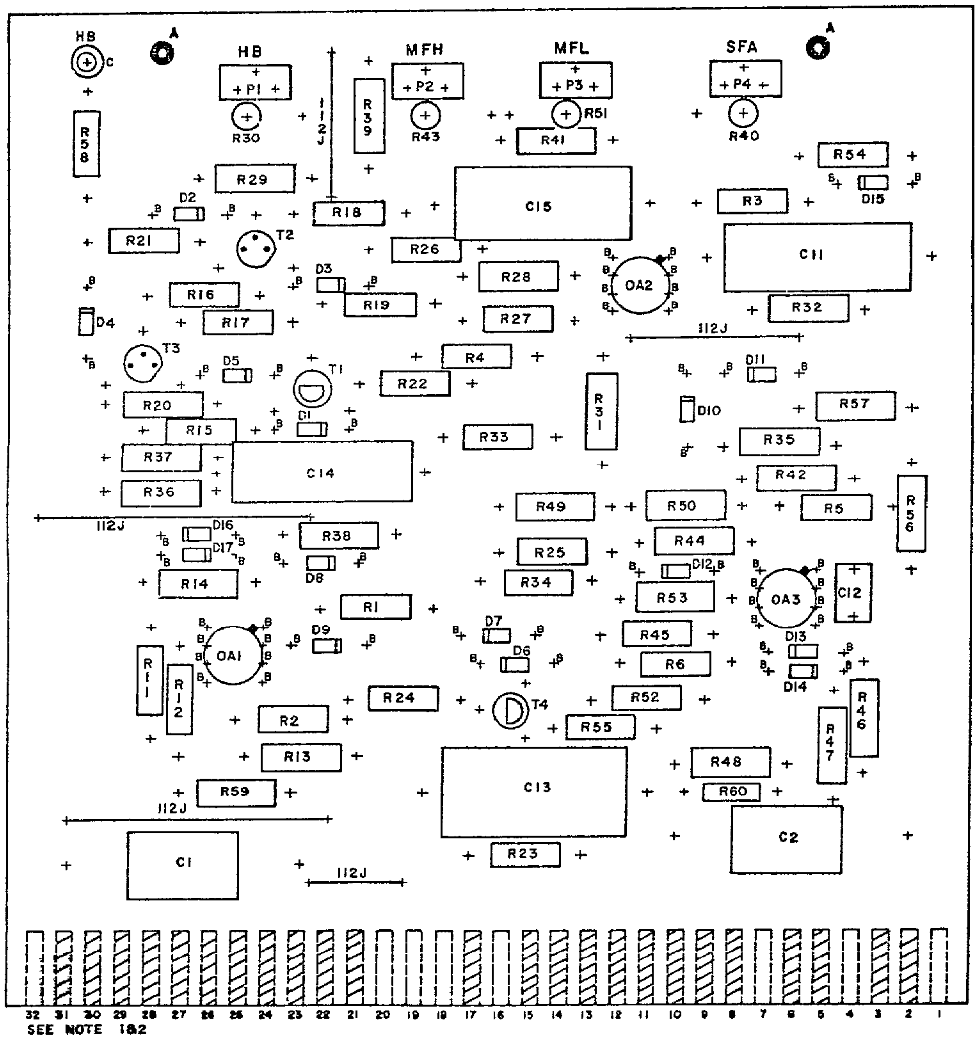

GROUP	KEY LOCATIONS		
G01	12 — 13	19 — 20	24 — 25

NOTES

1. INDICATED TAB NUMBERS CORRESPOND TO MATCHING RECEPTACLE NUMBERS
2. CROSS HATCHED TABS INDICATES TABS USED.
3. CARD SIZE, $5.500^{+.000}_{-.015}$ X $5.130^{+.002}_{-.008}$

TRANSISTOR LEAD SKETCHES

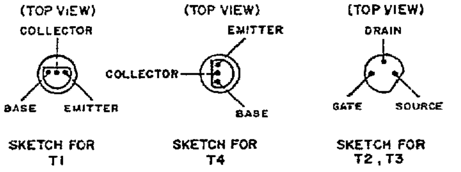

SKETCH FOR T1

SKETCH FOR T4

SKETCH FOR T2, T3

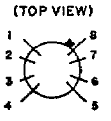

SKETCH FOR OA1, OA2, OA3

COMPONENT HEIGHT SKETCH

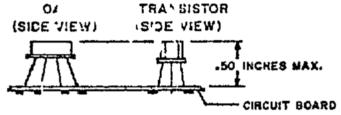

2X	36A358083AB004	—	1	—
SCALE	REAR ETCHED BOARD DWG.	FRONT ETCHED BOARD DWG.	FRONT	BACK
			SPACE UNIT REQUIREMENT	

REVISIONS

No revisions are to be made to this drawing without the specific approval of the Development Engineering Section of the Speed Variator Department

PRINTS TO

5B10	5J(RW)
5R12S	5TS(50)
5 10 CW	
SH 5	5X(BK)

MADE BY D Lanach FEB 7, 1964

ISSUED D Lanach MAY 8, 1964

APPROVALS

SPEED VARIATOR
ERIE

36C764190AB
CONT ON SHEET FL SH NO 2